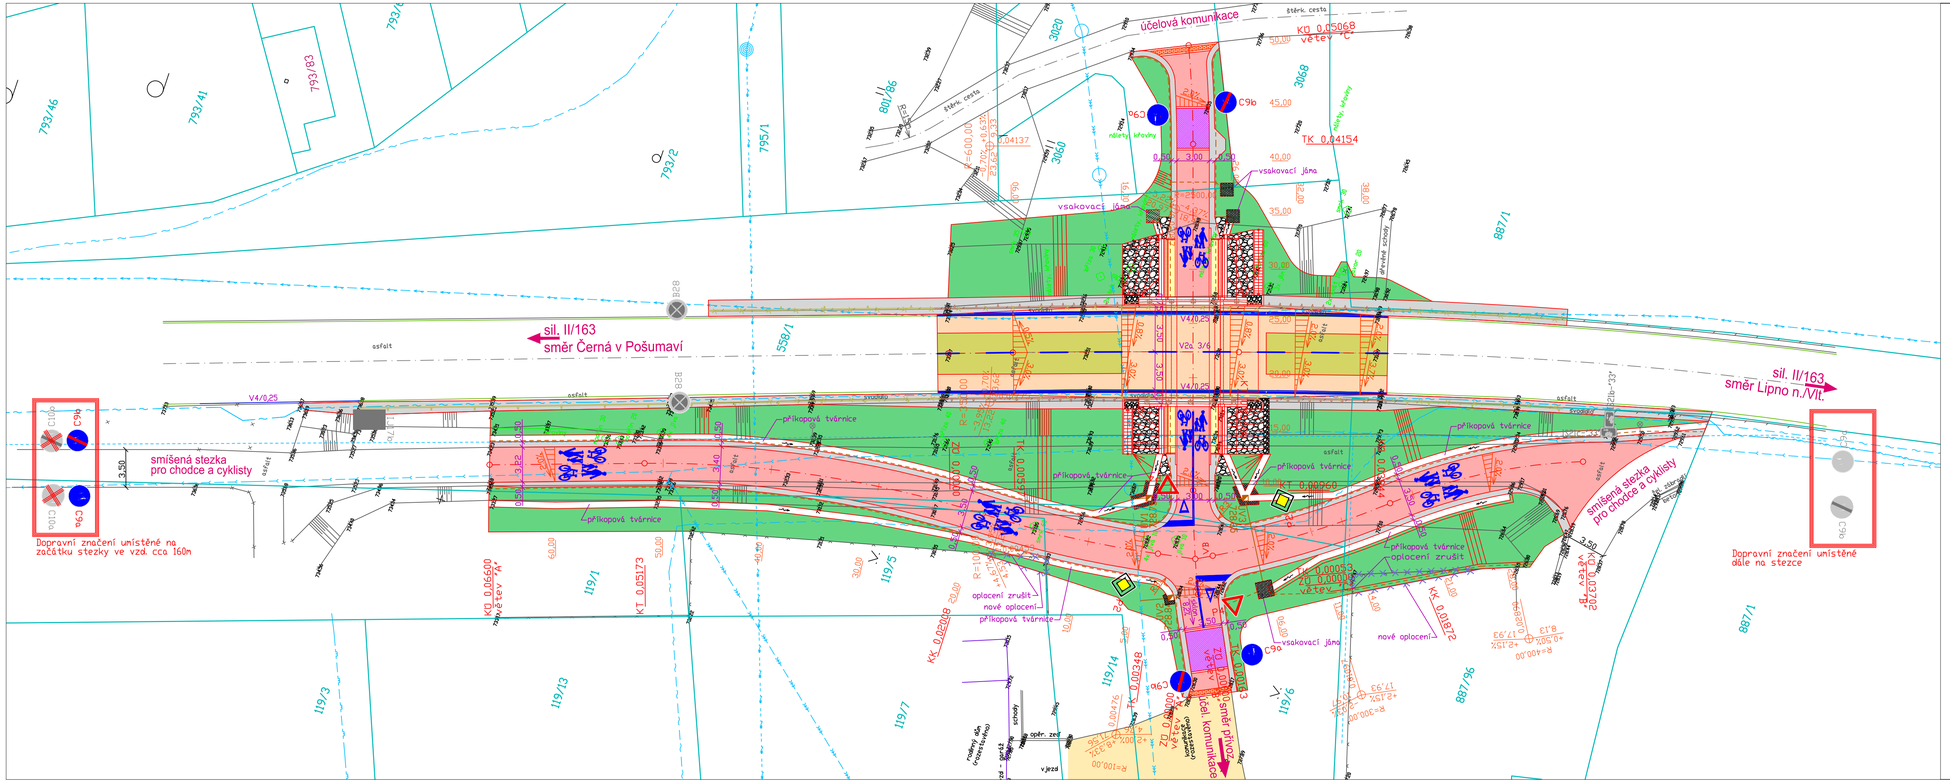

LEGENDA

- stávající hrany
- stávající vodorovné DZ
- navržené hrany
- hranice parcel KN
- proslouč. hranice parcel KN
- 887/1 čísla parcel KN
- 325 čísla stavebních parcel KN
- oplocení-rušené
- oplocení-navržené
- navržené vodorovné DZ
- P2 navržené svislé DZ
- C10a stávající svislé DZ-rušené
- C9a stávající svislé DZ
- navržené svodidlo
- stávající svodidlo
- stáv. svodidlo-rušené

Navržené plochy

- stezka pro chodce a cyklisty
- nová konstrukce vozovky sil. II/163
- nový kryt vozovky sil. II/163
- nezpevněná krajnice
- účelová komunikace-nezpevněný povrch (není součástí PD)
- betonová dlažba
- kamenná dlažba přejížděný práh
- zatravnění
- lomový kámen do beton. lože
- kamenné kostky do beton. lože
- vsakovací jáma/ povrch zatravněný
- reliefní dlažba

Inženýrské sítě

inž. sítě-stávající

- kanalizace
- kanalizace-výtlak
- vodovod
- STL plynovod
- VN kabel nadzemní
- sdělovací vedení podzemní
- veřejné osvětlení podzemní
- uliční vpust s přípojkou
- podélná drenáž

Výškový systém: B.p.v., Souřadnicový systém: S-JTSK

ZHOTOVITEL : ZESA s.r.o. L.B.Schneidera 414/2, 370 01 České Budějovice tel: +420 386 322 910, web: www.zesa.cz			AUTORIZAČNÍ RAZÍTKO :
KRESLIL : Ing. Jiří Kaška	ZODP. PROJEKTANT : Ing. Jiří Kaška	SCHVÁLIL : Ing. Radek Lukeš	
OBJEDNATEL : EUROVIA CZ a.s., závod Č.Budějovice, Planá 72, Č.Budějovice		STUPEŇ DOK. :	RDS
PROJEKT : Podchod pro pěší a cyklisty pod silnicí II/163, Frymburk		Č. ZAKÁZKY :	20/16
		DATUM :	1/2025
		FORMÁT :	5xA4
		MĚŘÍTKO :	1:250
OBJEKT :		Č. PŘÍLOHY :	Č. PARÉ :
PŘÍLOHA : Situace		C.4	